



WOHNFLÄCHE FÜR EINE WOHNHEIT
NACH DIN 283 = 105.09 M²


DACHNEIGUNG: $\alpha = 32^\circ$
DACHEINDECKUNG: FRANKFURTER PFANNE, DUNKELBRAUN
KAMINKÖPFE: KLINKER GEFÜGT
AUßENMAUERWERK: KELLER: KSV - 150, 24 CM STARK
GESCHOSSE: HLZ - 150, DIN 105, OD. HBL DIN 18151, 30 CM STARK
DECKENISOL.: 20/25 MM GERRIX-DÄMMFILZ, 35MM BETONESTRICH
WAAGR. ISOL.: BITUMENPAPPE 500ER, SENKR. ISOL.: ZEMENTMORTELPUTZ MV. 1:3 GEGL.U.
2 X INERTOLANSTRICH
ROLLÄDEN AN FENSTERN UND FENSTERTÜREN!

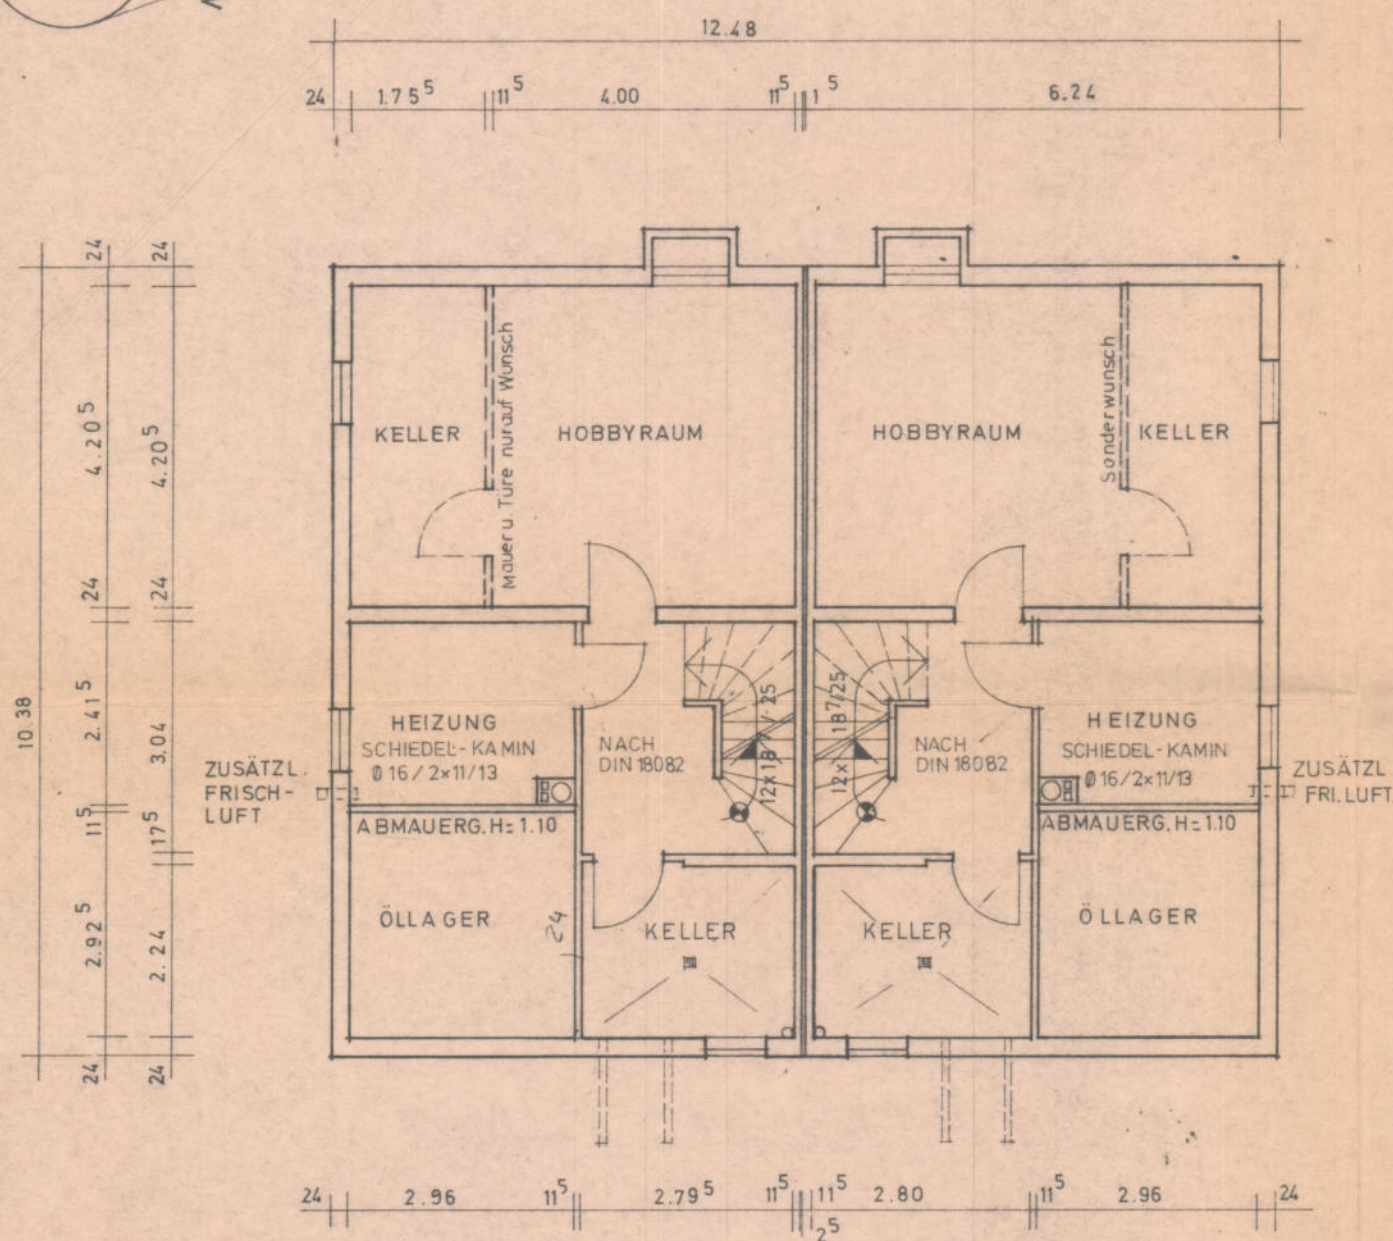


KELLERGESSCH

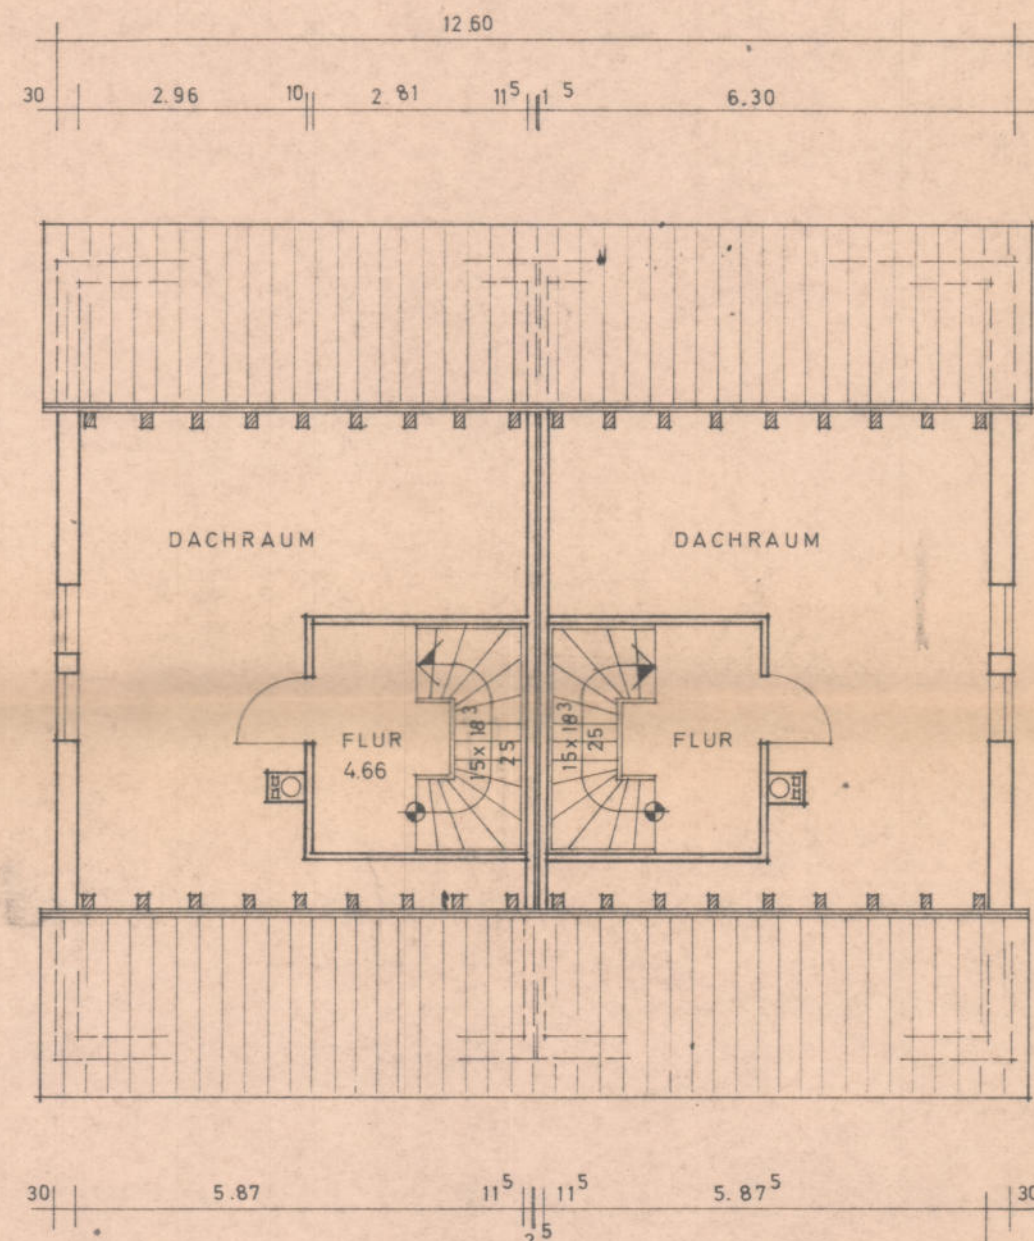


DACHGESCH

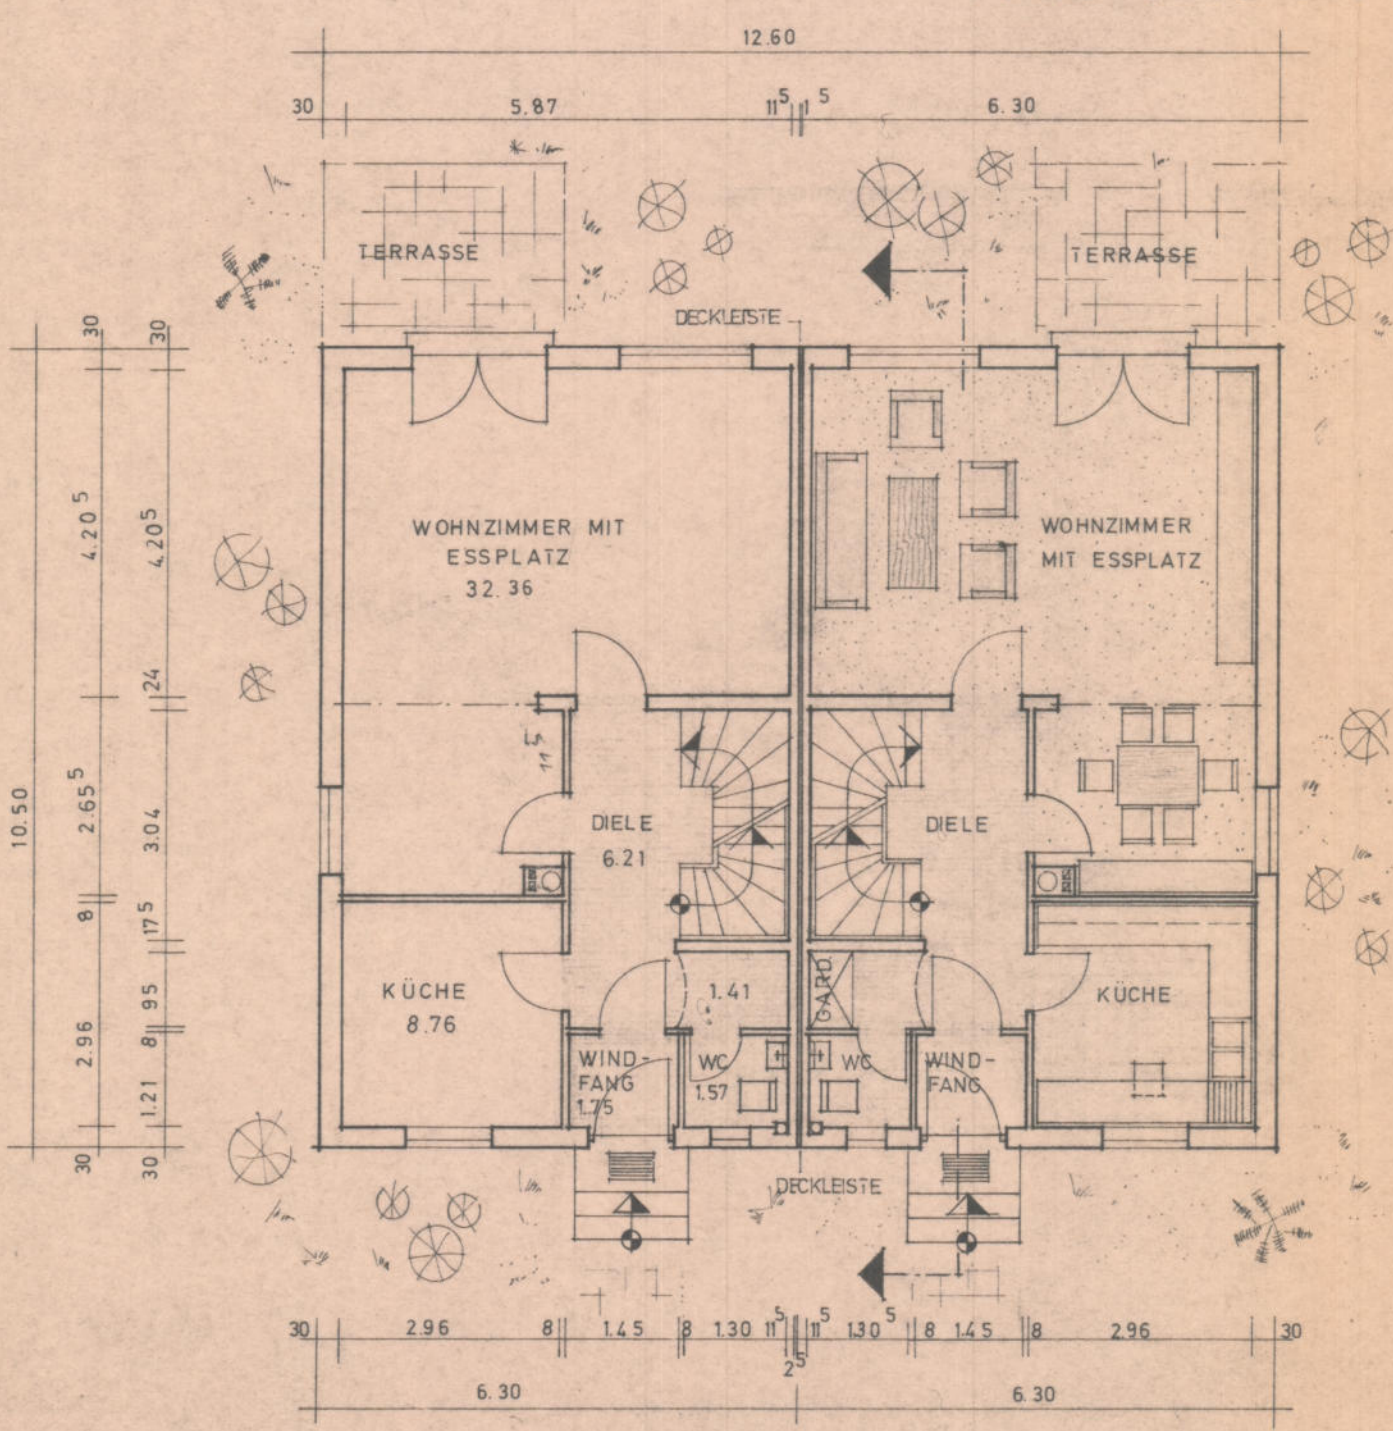

ERDGESCH

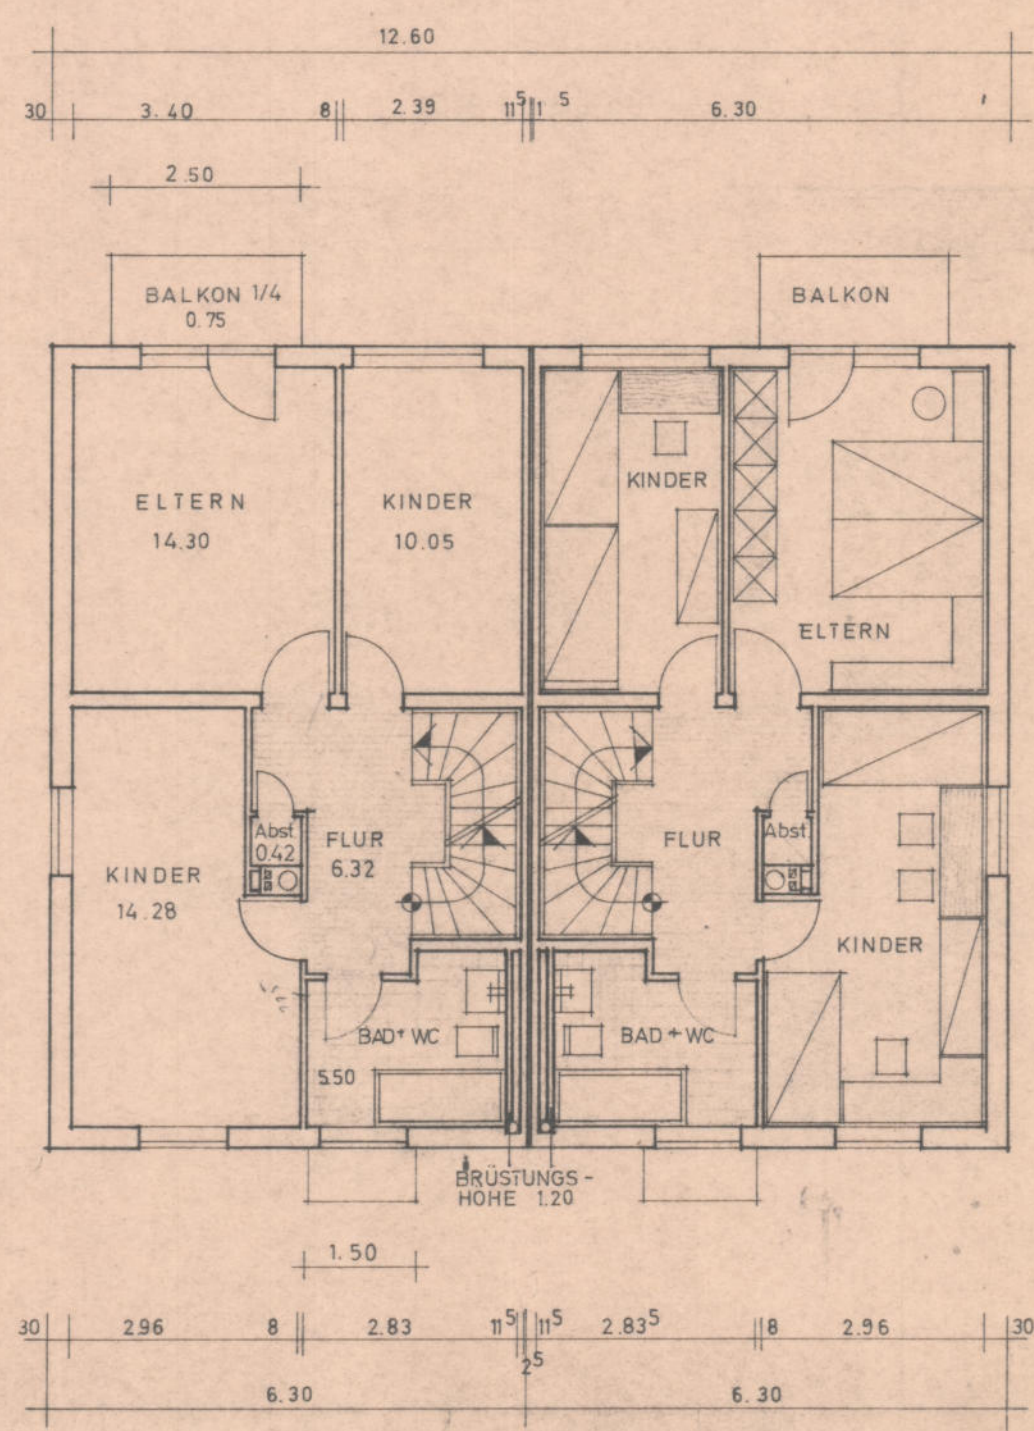

OBERGESCH

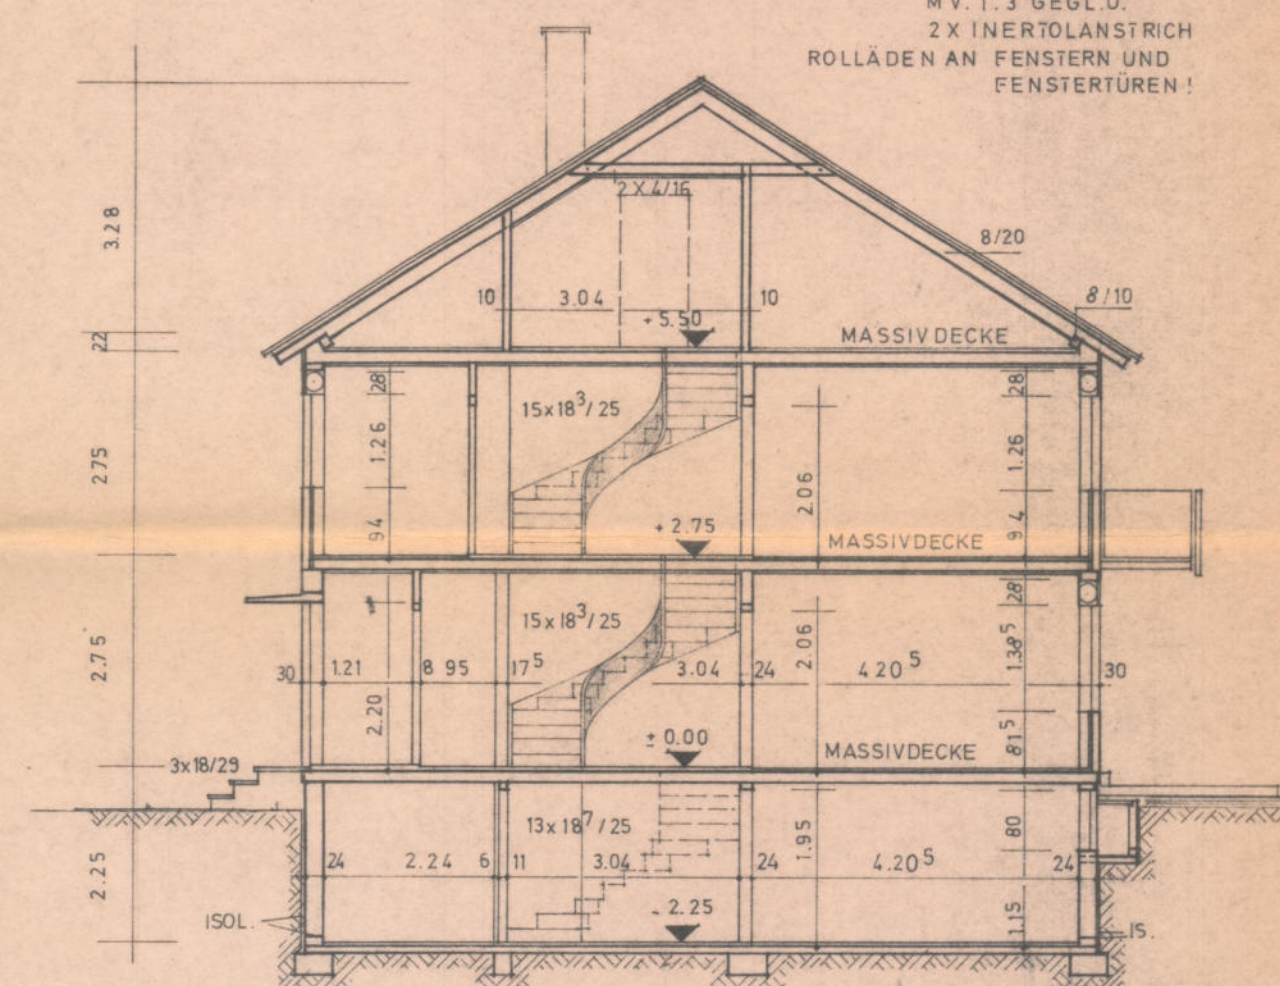

technisch geprüft

Forchheim, den 9. AUG. 1971

Kreisbaumeister

(Riedberger)

Kreisoberbaurat

SCHNITT

HANS MAUSS
Hochbau Tiefbau Stahltonbau

DER BAUHERR:

DIE NACHBARN:

TYP R 630

NEUBAU VON 6 DOPPELWOHNHÄUSERN

KELLER - ERD - OBER - DACHGESCH, SCHNITT, M=1:100

BAUORT: KERSBACH, KRS. FORCHHEIM
FL.-NR. 212, 212/1, 213, 213/1, 214, 214/1

Genehmigt mit Bescheid

vom 9. AUG. 1971

Nr. 11/15 6021-BAUHERR:

Landratsamt Forchheim

FA. HANS MAUSS, BAUUNTERNEHMEN,
NEHMEN, 852 ERLANGEN,
SIEMENSSTR. 41, TEL. 25091

Handwritten signature of Hans Mauss


FA. HANS MAUSS, BAUUNTERNEHMEN, ERLANGEN,
SIEMENSSTR. 41, TEL. 25091

Hochbau Tiefbau Stahltonbau


ERLANGEN

ERLANGEN, DEN 22.3.1971

TEKTURPLAN

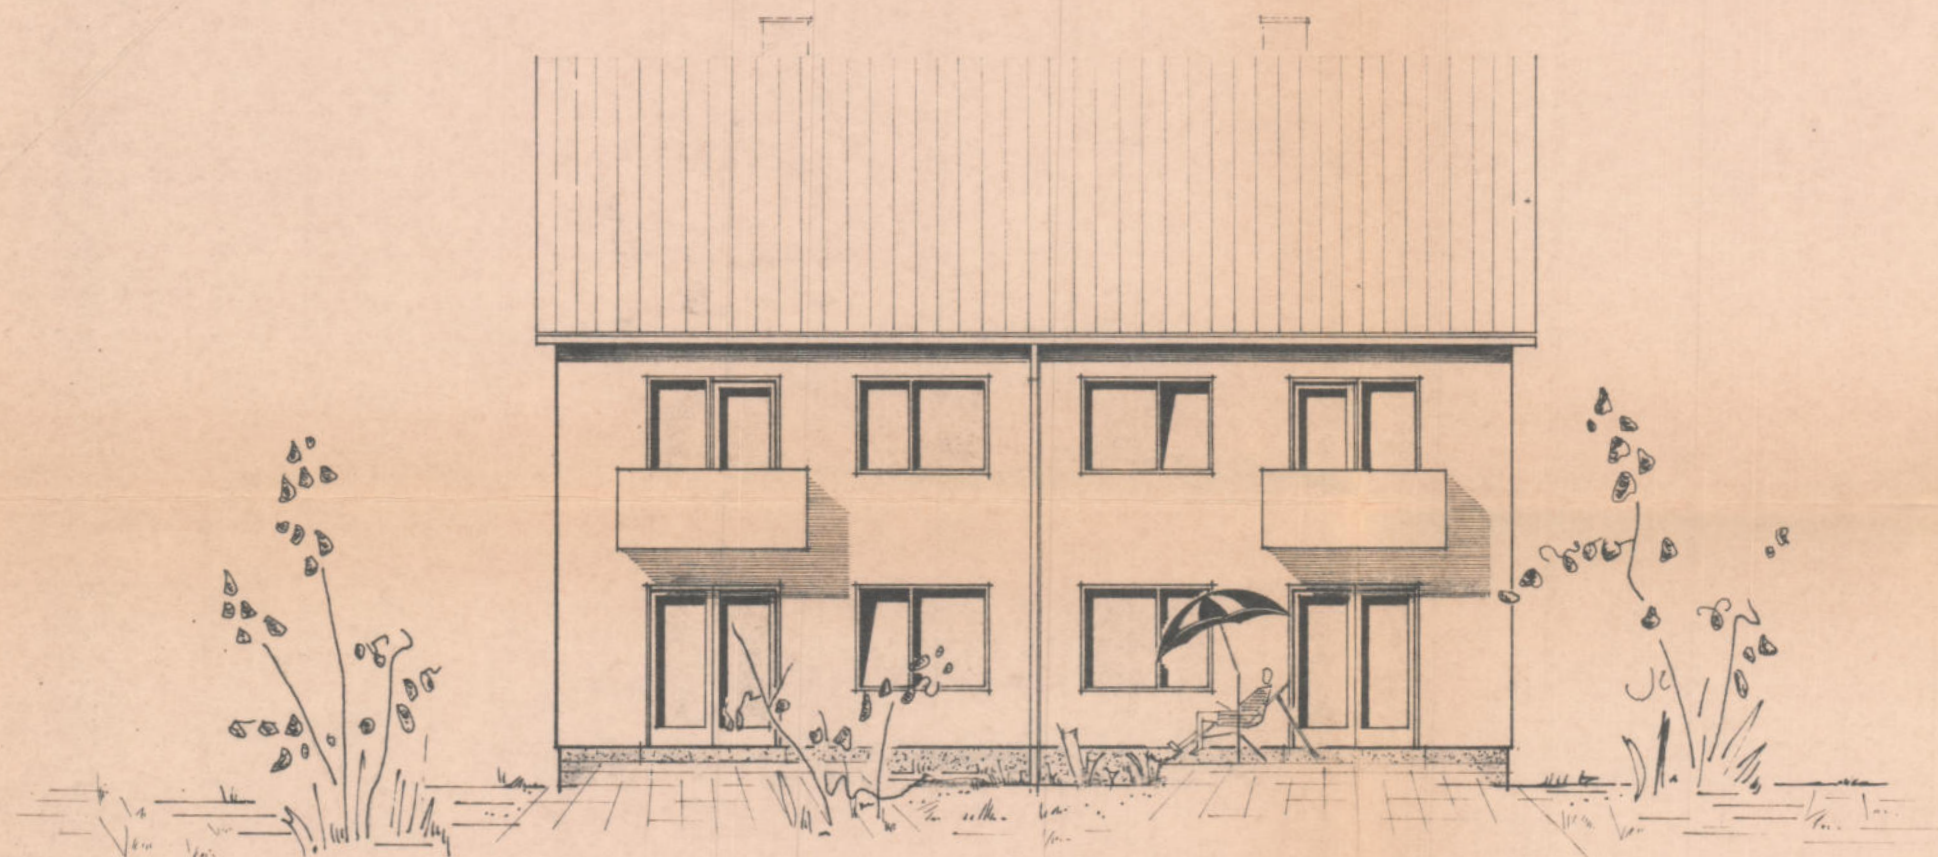

S Ü D - W E S T E N

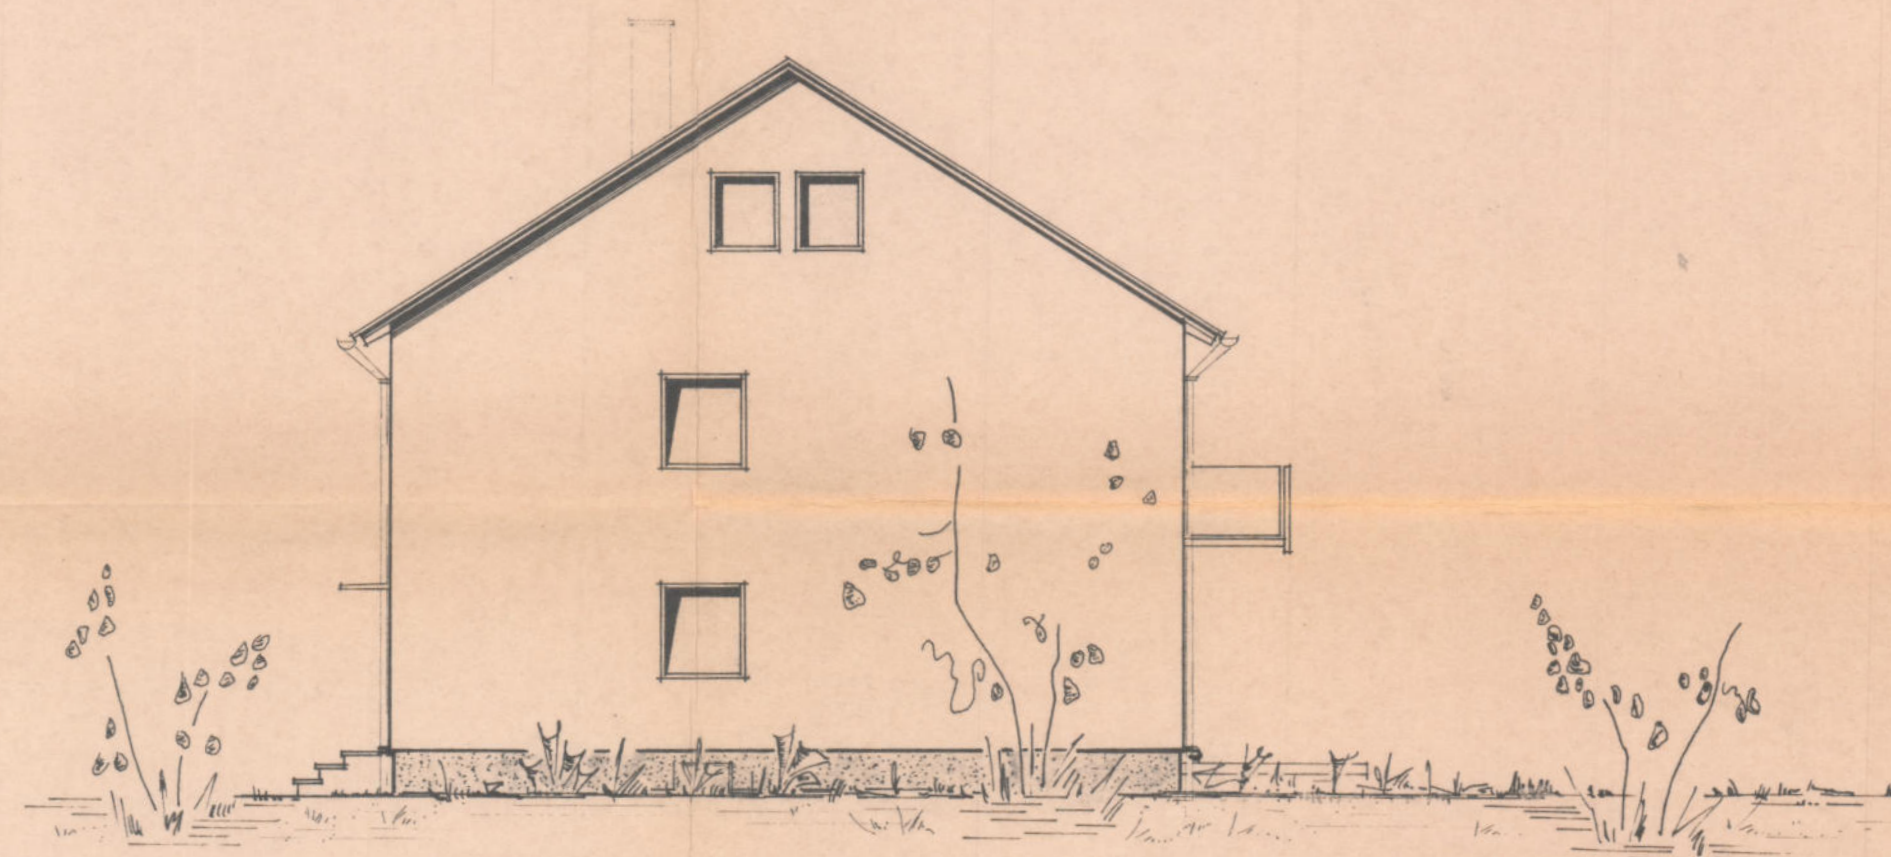

N O R D - W E S T E N

Technisch geprüft

Forchheim, den 9. AUG. 1971

Kreisbaumeister

(Riedlberger)

Kreisoberbaurat

DER BAUHERR:

DIE NACHBARN:

HANS MAUSS
Hochbau Tiefbau Stahlbetonbau
ERLANGEN

TYP R 630


NEUBAU EINES DOPPELWOHNHAUSES

ANSICHTEN


M = 1:100

BAUORT : KERSBACH, KRS. FORCHHEIM
FL-NR. 212, 212/1, 213, 213/1, 214, 214/1

BAUHERR : FA. HANS MAUSS, BAUUNTER-
NEHMEN, 852 ERLANGEN,
SIEMENSSTR. 41, TEL. 25091

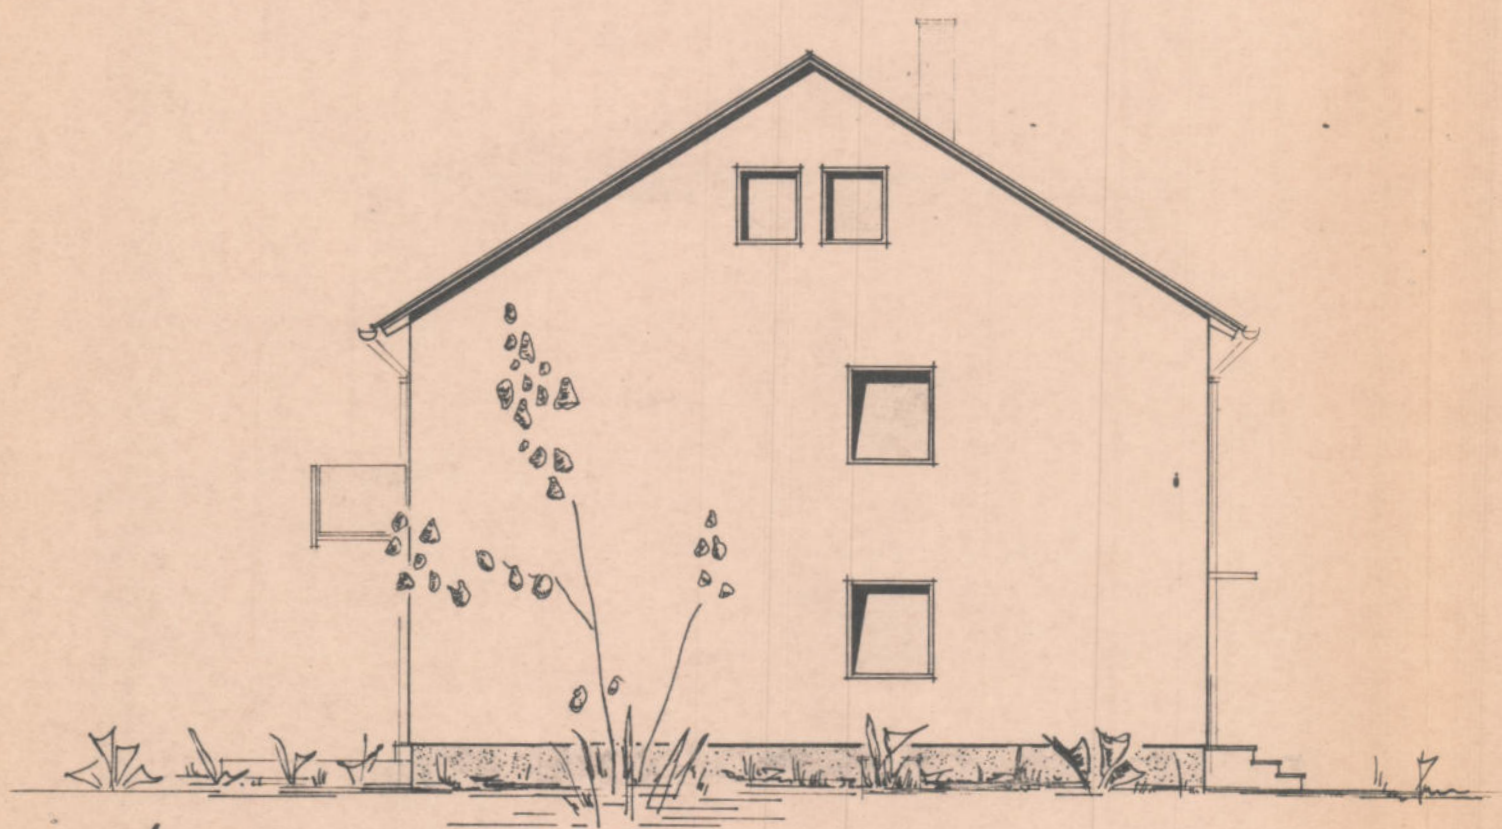

S Ü D - O S T E N

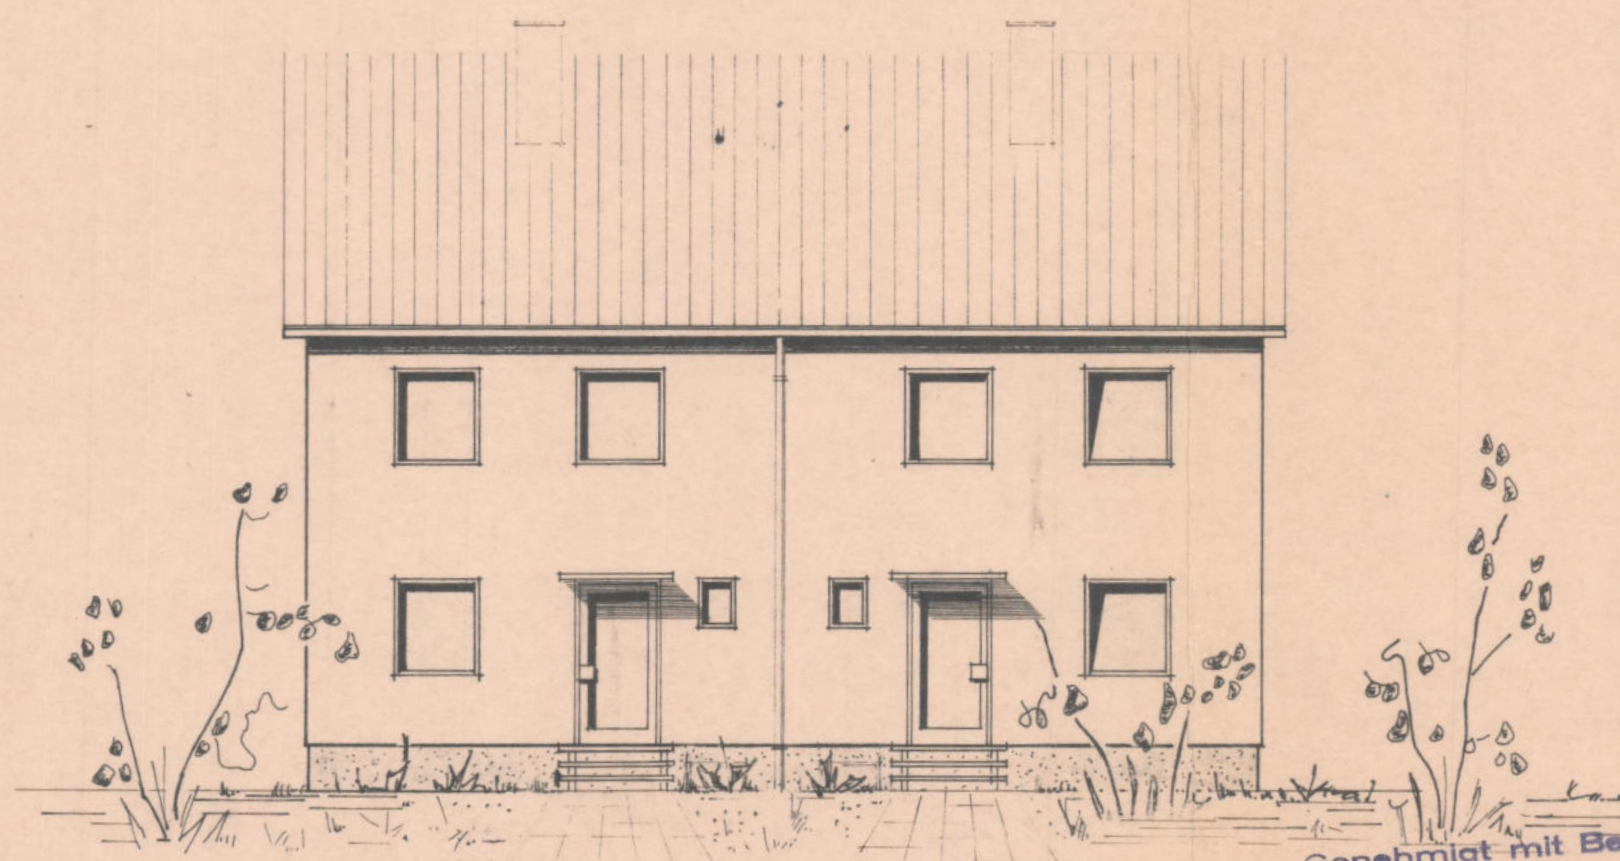

N O R D - O S T E N

Genehmigt mit Bescheid

vbm 9. AUG. 1971

Nr. 11/15 6021-

Landratsamt Forchheim

HANS MAUSS, BAUUNTERNEHMEN, ERLANGEN,
SIEMENSSTR. 41, TEL. 25091


Hochbau Tiefbau Stahlbetonbau

ERLANGEN

ERLANGEN, DEN 27.3.1971


(Ammon)
Landrat

TEKTURPLAN

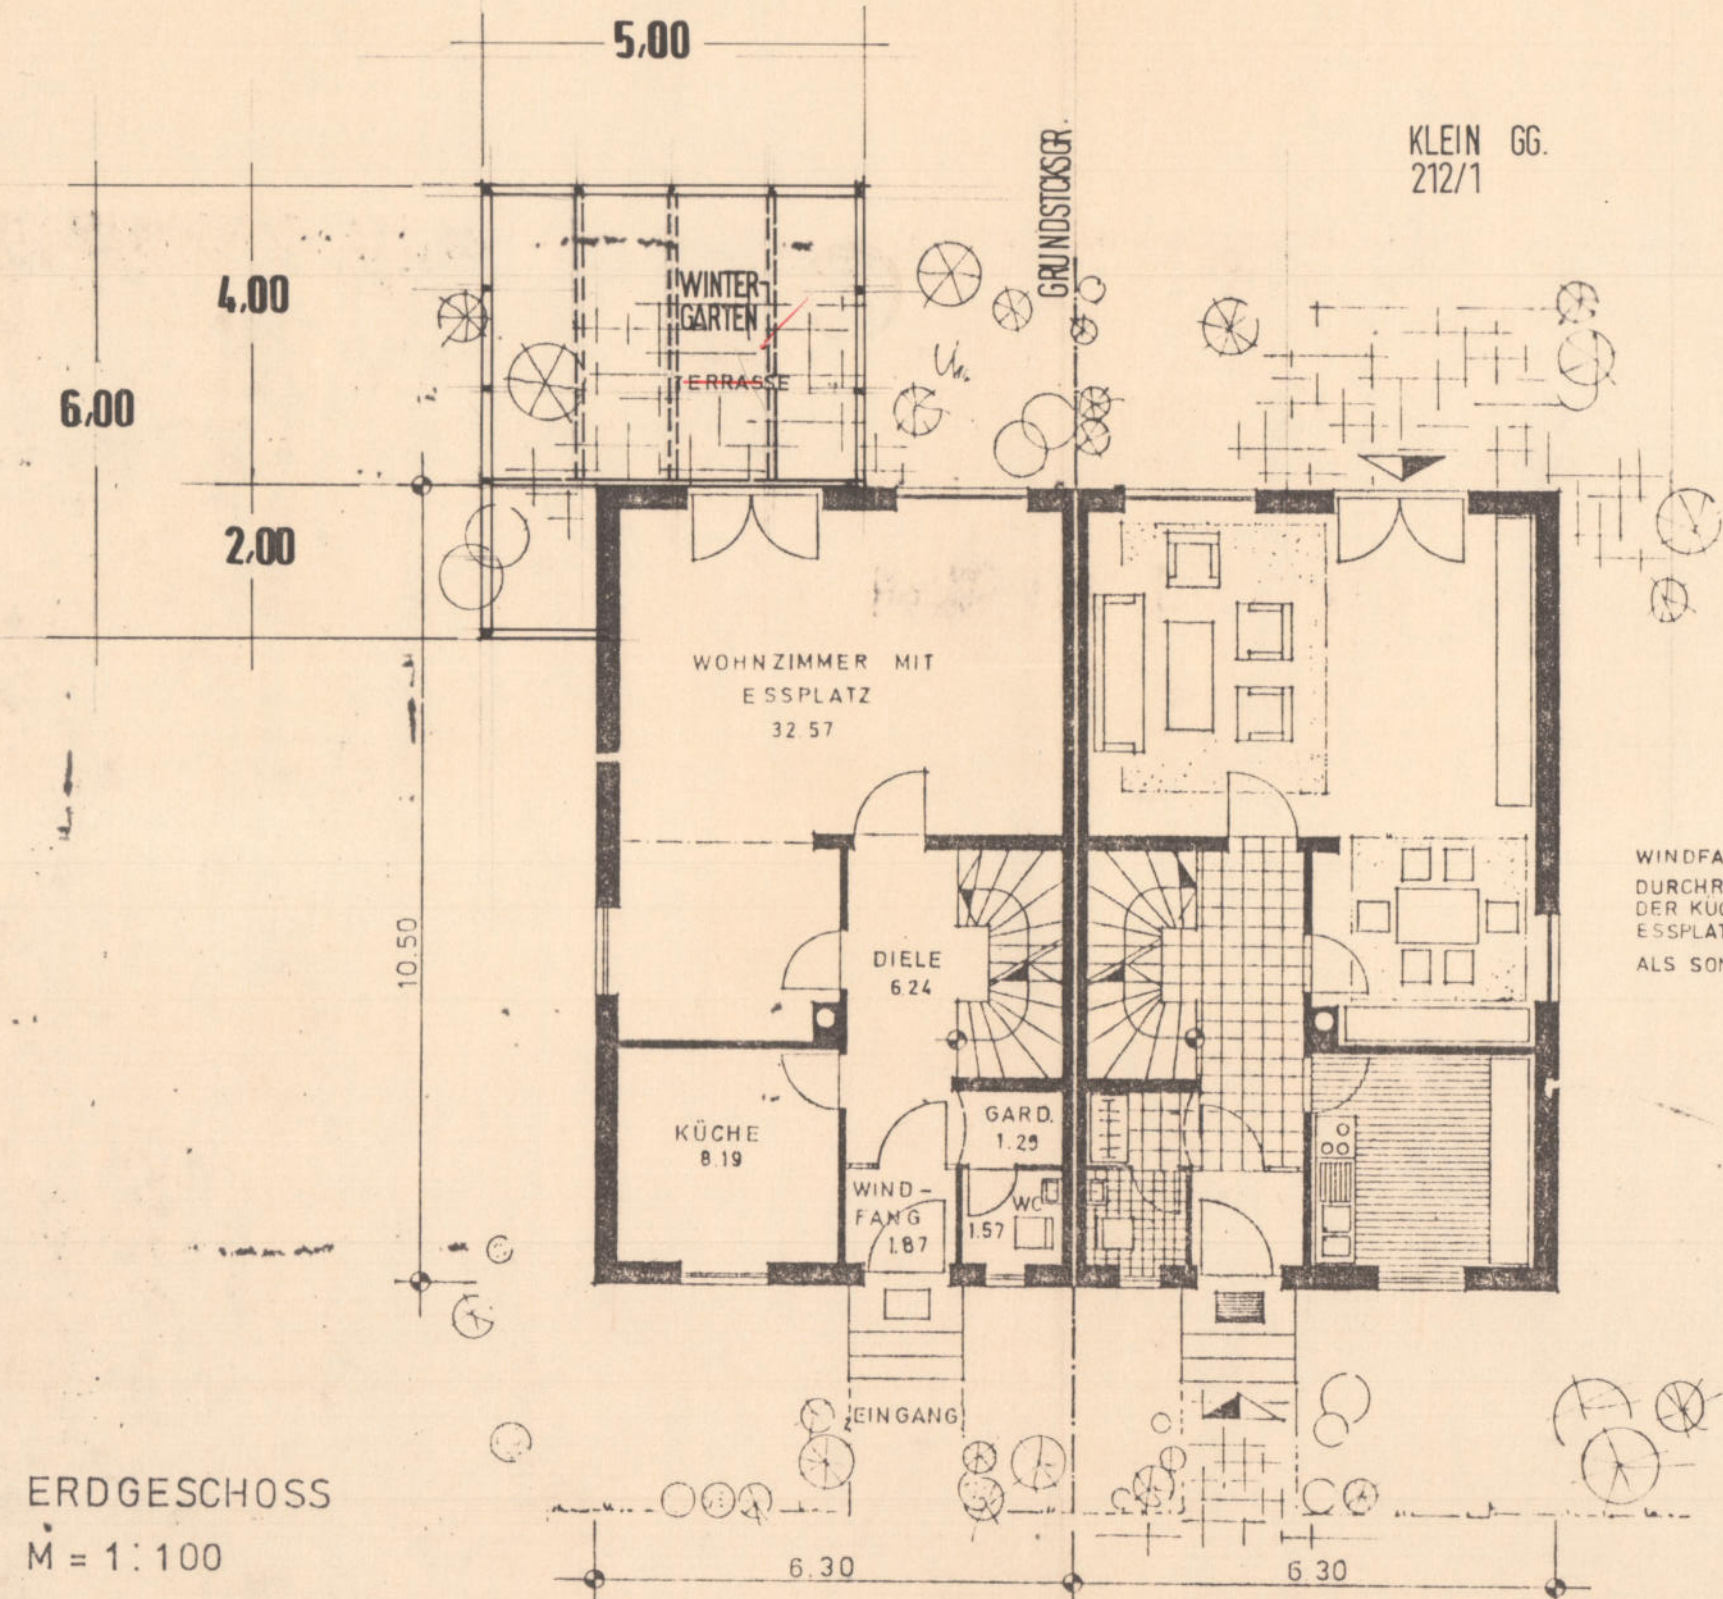

WINDFANGTÜR
DURCHREICHE VON
DER KÜCHE ZUM
ESSPLATZ
ALS SONDERWUNSCH

ANSICHT WEST
M = 1:100

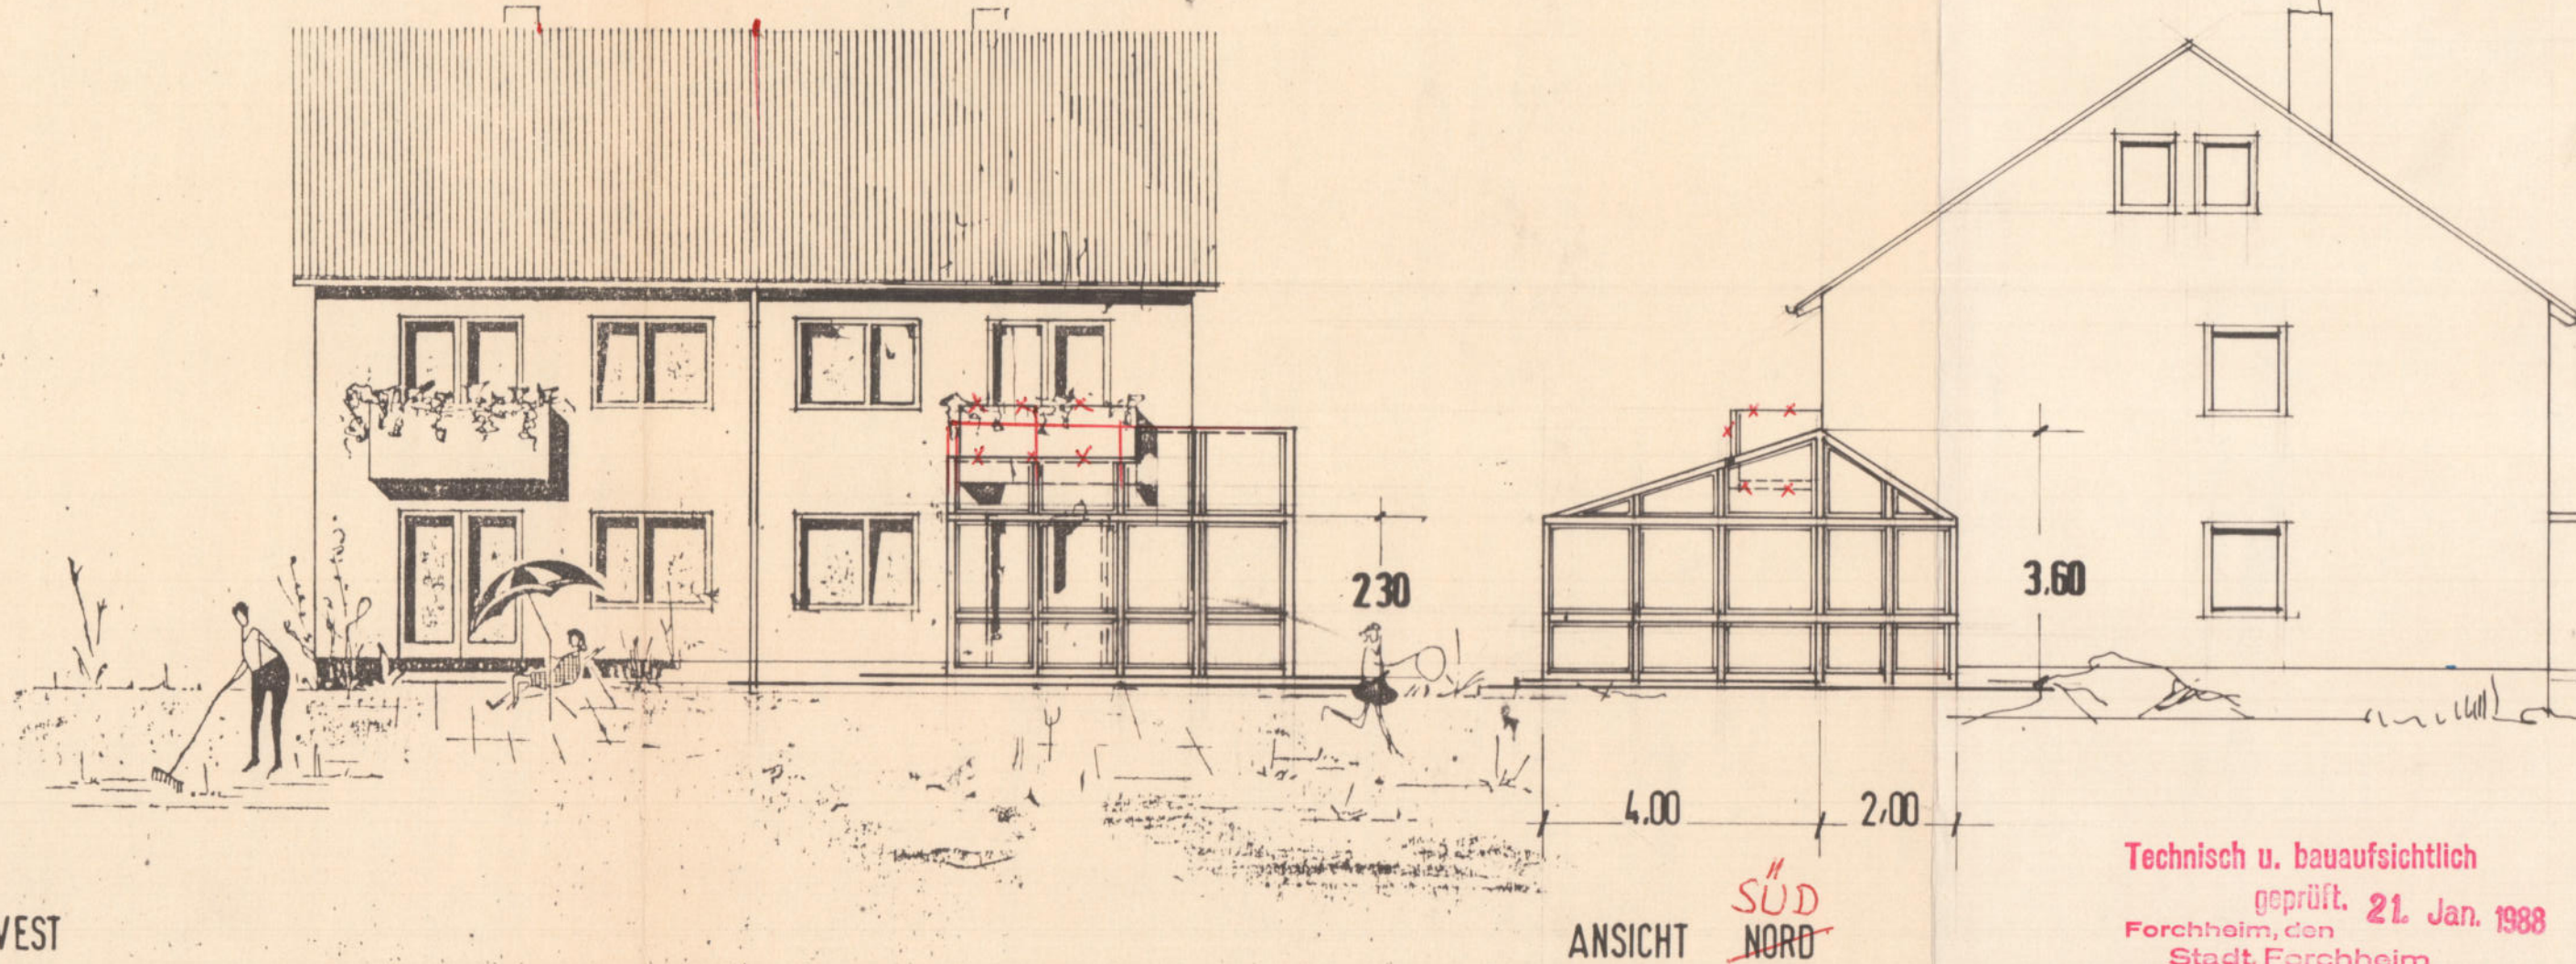

Technisch u. bauaufsichtlich
geprüft. 21. Jan. 1988

Forchheim, den
Stadt Forchheim
- Stadtbauamt -
im Auftrag

GENEHMIGUNGSVERMERK

Genehmigt aufgrund des
Baugenehmigungsbescheides
vom 25.1.88 Baubuch-Nr. 413/87-K
Forchheim, 27. JAN. 1988

STADT FORCHHEIM
- Stadtbauamt -
im Auftrag

EINGABEPLAN
ZUR ERRICHTUNG
EINES
WINTERGARTENS
BAUHERR: PETER BEVERLE

BIRKENWEG 8
8550 FORCHHEIM

FL. NR. 212/14 GEMARK. KERSBACH

NACHBARN:

- ① FL. NR. 212/15 *W. W.*
- ② FL. NR. 212 *E. W.*
- ③ FL. NR. 212/1 *W. W.*
- ④ FL. NR. 213 *M. B.*
- ⑤ FL. NR. 213/1 *J. R.*

BAUHERR: *Beverle*

PLANUNG:
S. König
DIETER KÖNIG

Erweiterung des Goldstandes (Güterpunkte)

$$5,00 \times 4,00 = 20,00$$

$$1,50 \times 2,00 = 3,00$$

$$23,00$$

